

LEGAL DESCRIPTION

(PER STATUTORY WARRANTY DEED RECORDING# 20201106002012)

LOT 22 IN BLOCK 38 OF CAPITOL HILL ADDITION DIVISION NO. 5, AS PER PLAT RECORDED IN VOLUME 12 OF PLATS, PAGE 23, RECORDS OF KING COUNTY AUDITOR;

SITUATE IN THE CITY OF SEATTLE, COUNTY OF KING, STATE OF WASHINGTON.

BASIS OF BEARINGS

AN ASSUMED BEARING OF N 00°09'11" E WAS HELD BETWEEN SURVEY MONUMENTS FOUND ON THE CENTERLINE OF 19TH AVE. E.

REFERENCES

- R1 CAPITOL HILL ADD'N, DIV. 5, RECORDED IN VOL. 12 OF PLATS, PG. 23.
R2 RECORD OF SURVEY, RECORDED IN BK. 155 OF SURVEYS, PG. 215.
ALL IN RECORDS OF KING COUNTY, WASHINGTON.

VERTICAL DATUM

NAVD(88) PER GPS OBSERVATIONS.

SURVEYOR'S NOTES


1. THE TOPOGRAPHIC SURVEY SHOWN HEREON WAS PERFORMED IN JANUARY OF 2021. THE FIELD DATA WAS COLLECTED AND RECORDED ON MAGNETIC MEDIA THROUGH AN ELECTRONIC THEODOLITE. THE DATA FILE IS ARCHIVED ON DISC OR CD. WRITTEN FIELD NOTES MAY NOT EXIST. CONTOURS ARE SHOWN FOR CONVENIENCE ONLY. DESIGN SHOULD RELY ON SPOT ELEVATIONS.
2. ALL MONUMENTS SHOWN HEREON WERE LOCATED DURING THE COURSE OF THIS SURVEY UNLESS OTHERWISE NOTED.
3. THE TYPES AND LOCATIONS OF ANY UTILITIES SHOWN ON THIS DRAWING ARE BASED ON INFORMATION PROVIDED TO US, BY OTHERS OR GENERAL INFORMATION READILY AVAILABLE IN THE PUBLIC DOMAIN INCLUDING, AS APPLICABLE, IDENTIFYING MARKINGS PLACED BY UTILITY LOCATE SERVICES AND OBSERVED BY TERRANE IN THE FIELD. AS SUCH, THE UTILITY INFORMATION SHOWN ON THESE DRAWINGS ARE FOR INFORMATIONAL PURPOSES ONLY AND SHOULD NOT BE RELIED ON FOR DESIGN OR CONSTRUCTION PURPOSES; TERRANE IS NOT RESPONSIBLE OR LIABLE FOR THE ACCURACY OR COMPLETENESS OF THIS UTILITY INFORMATION. FOR THE ACCURATE LOCATION AND TYPE OF UTILITIES NECESSARY FOR DESIGN AND CONSTRUCTION, PLEASE CONTACT THE SITE OWNER AND THE LOCAL UTILITY LOCATE SERVICE (800-424-5555).
4. SUBJECT PROPERTY TAX PARCEL NO. 133830-0625.
5. SUBJECT PROPERTY AREA PER THIS SURVEY IS 4,317 ±S.F. (0.10 ACRES)
6. THIS SURVEY WAS PERFORMED WITHOUT THE BENEFIT OF A TITLE REPORT. EASEMENTS AND OTHER ENCUMBRANCES MAY EXIST THAT ARE NOT SHOWN HEREON.
7. FIELD DATA FOR THIS SURVEY WAS OBTAINED BY DIRECT FIELD MEASUREMENTS WITH A CALIBRATED ELECTRONIC 5-SECOND TOTAL STATION AND/OR SURVEY GRADE GPS OBSERVATIONS. ALL ANGULAR AND LINEAR RELATIONSHIPS ARE ACCURATE AND MEET THE STANDARDS SET BY WAC 332-130-090.

LEGEND


	AREA DRAIN		GAS METER
	ASPHALT SURFACE		NAIL AS NOTED
	BRICK SURFACE		POWER METER
	BUILDING		POWER (OVERHEAD)
	CENTERLINE ROW		POWER POLE W/ LIGHT
	CONCRETE SURFACE		REBAR & CAP (SET)
	RETAINING WALL		ROCKERY
	DECK		SEWER LINE
	FENCE LINE (CHAIN LINK)		SEWER MANHOLE
	FENCE LINE (WOOD)		TREE (AS NOTED)
	MONUMENT IN CASE (FOUND)		WATER METER

VICINITY MAP

N.T.S.

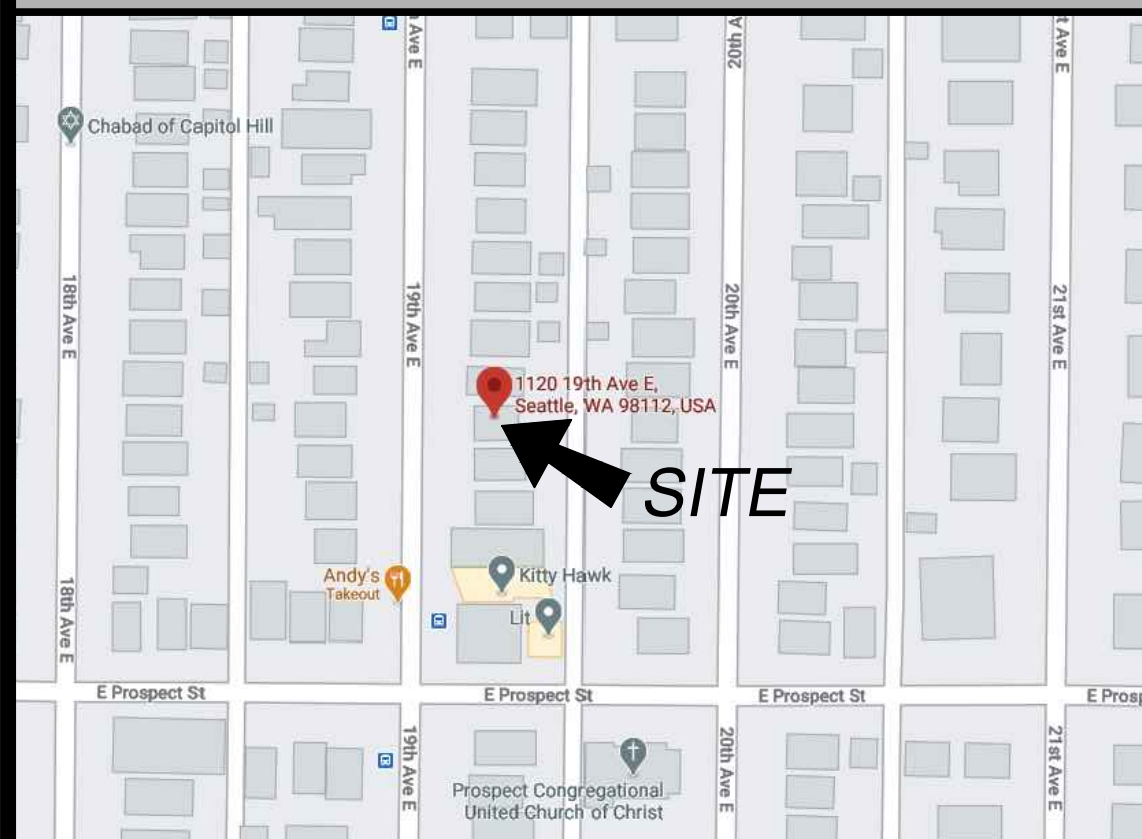

TOPOGRAPHIC & BOUNDARY SURVEY

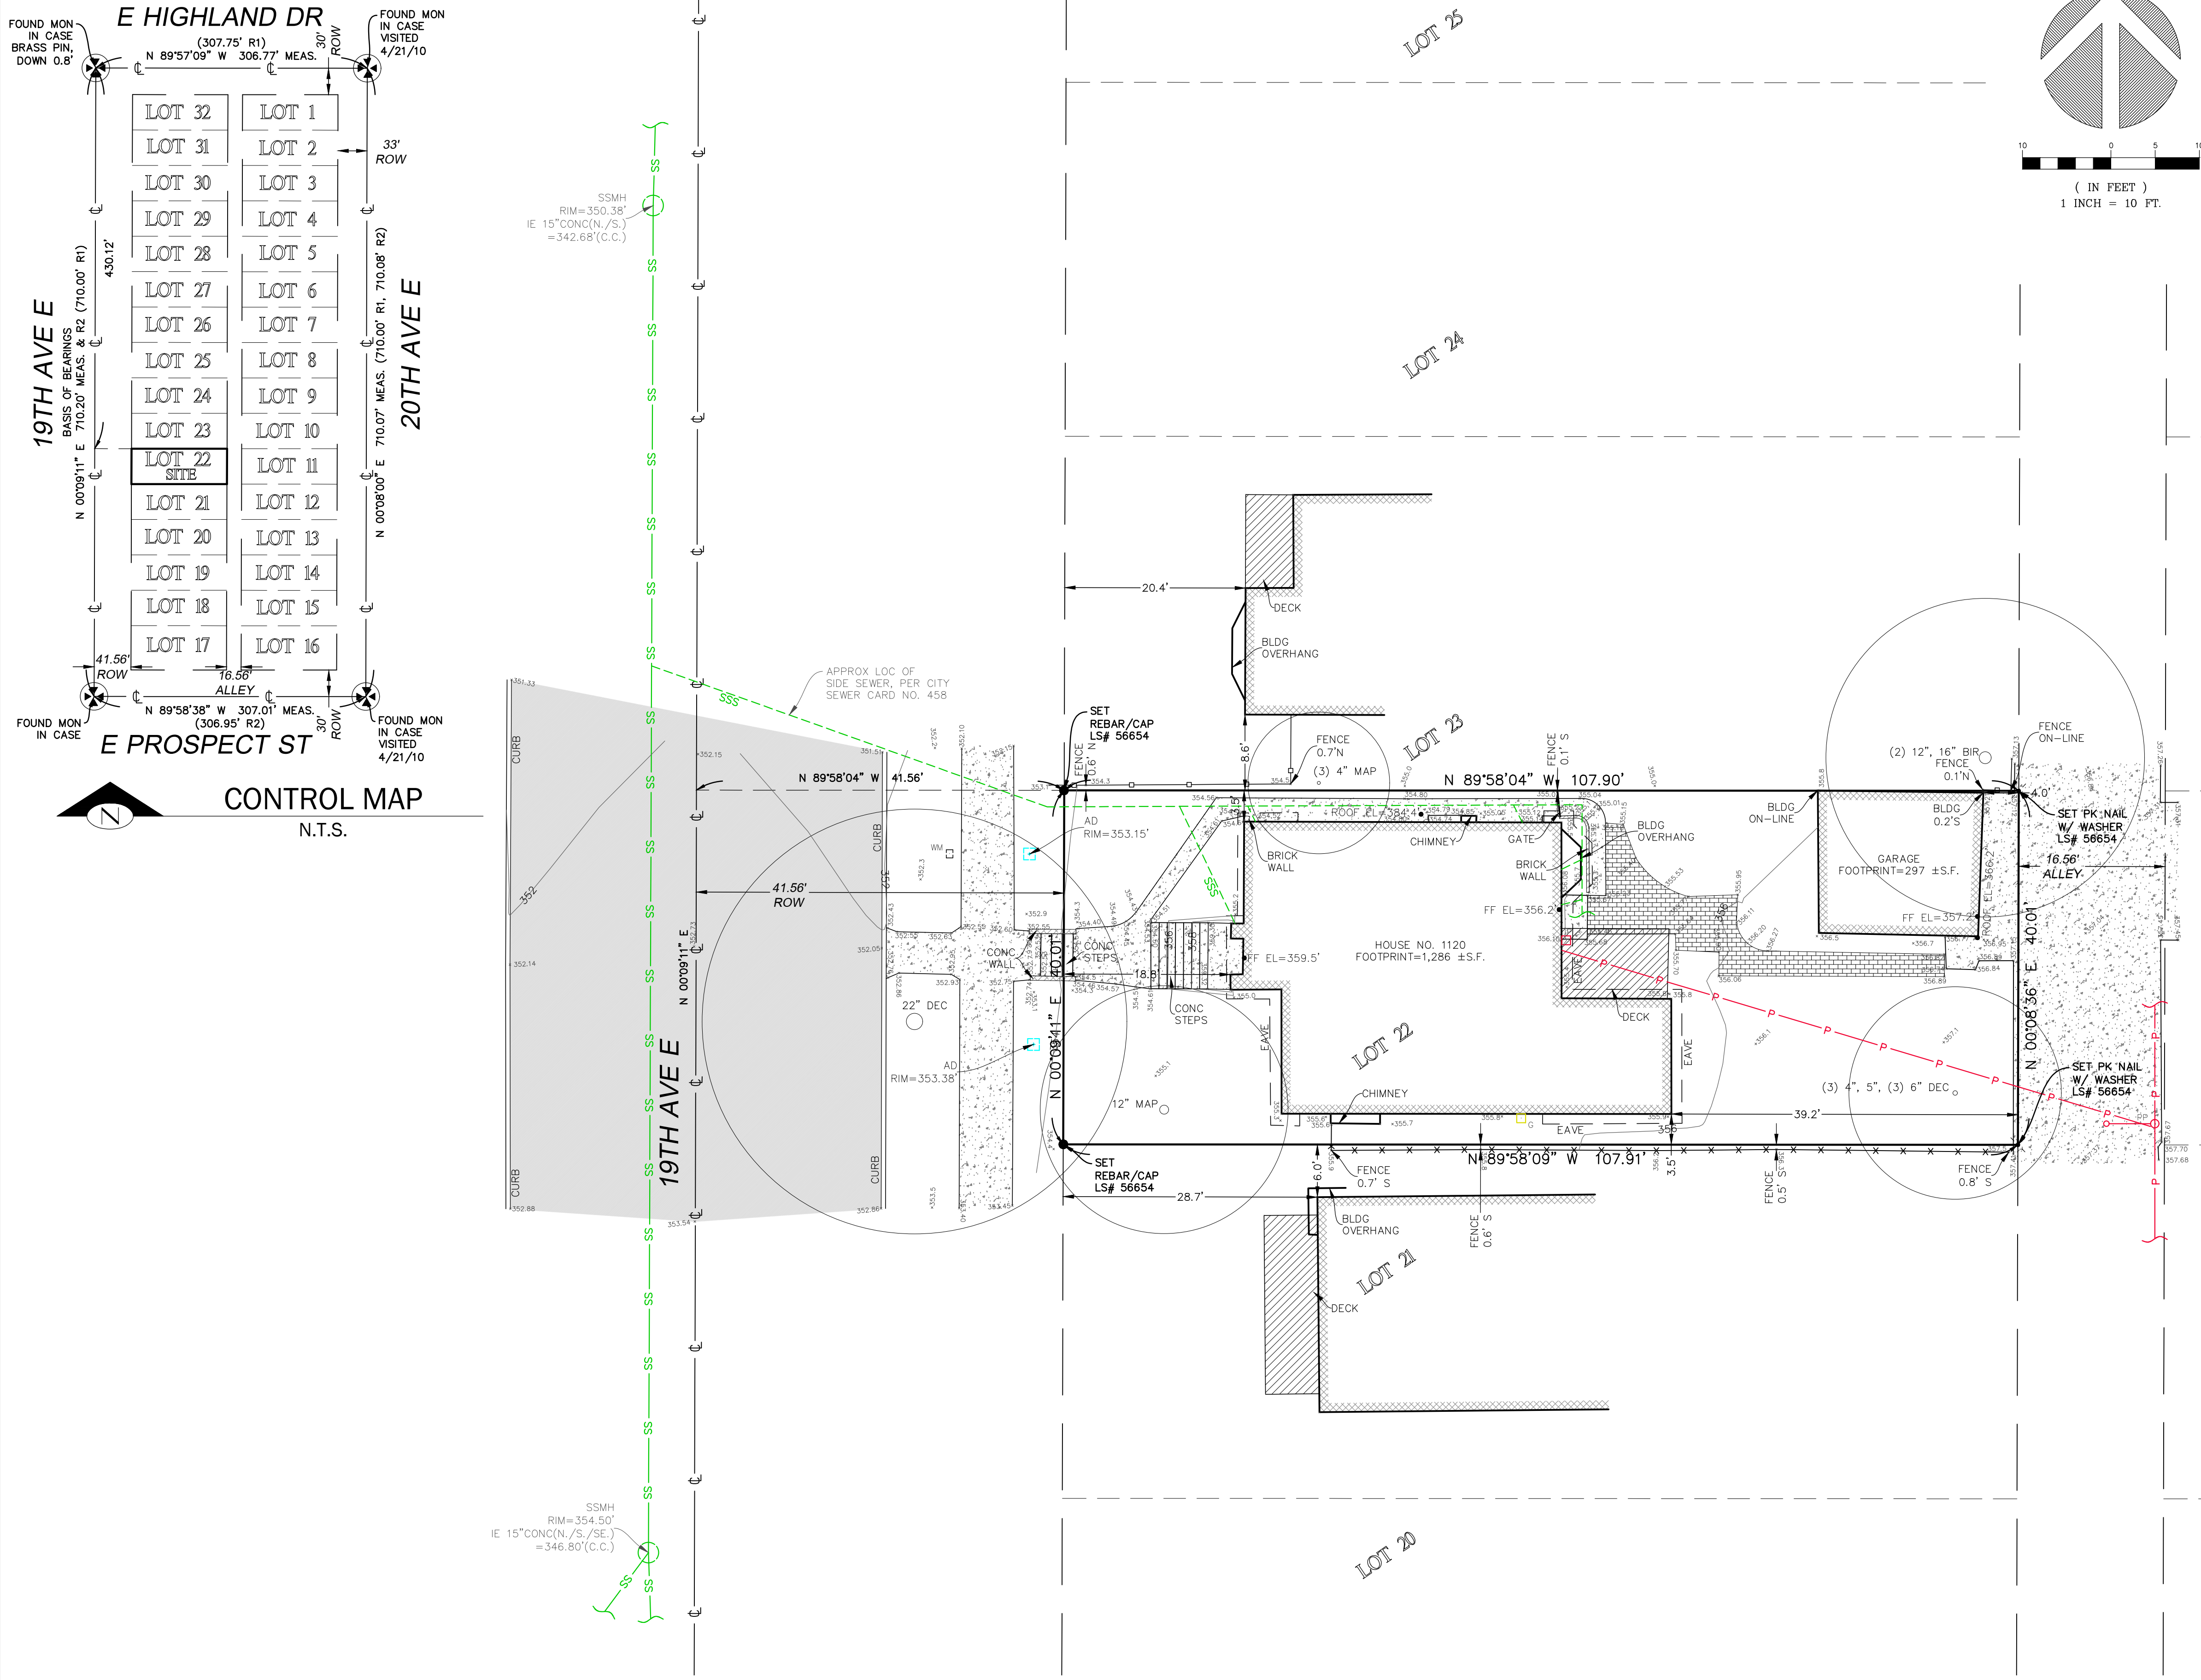

INDEXING INFORMATION			
NE	1/4	NW	1/4
SW	4	SE	4
SECTION: 28			
TOWNSHIP: 25N			
RANGE: 04E, W.M.			
COUNTY: KING			

TOPOGRAPHIC & BOUNDARY SURVEY

PARCEL NO. 1338300625

MICKLOS RESIDENCE

1120 19TH AVE E
SEATTLE, WA 98112



Terrane
10801 Main Street, Suite 102, Bellevue, WA 98004
phone 425.458.4498 support@terrane.net
www.terrane.net

JOB NUMBER:	202558
DATE:	01/22/21
DRAFTED BY:	IDV-GKD
CHECKED BY:	JGM/RLS
SCALE:	1" = 10'

REVISION HISTORY

NO.	DESCRIPTION	DATE

SHEET NUMBER

1 OF 1